


HOSSZMETSZET M 1:100


[]-es értékek mérőleges hosszak

(α=70°)

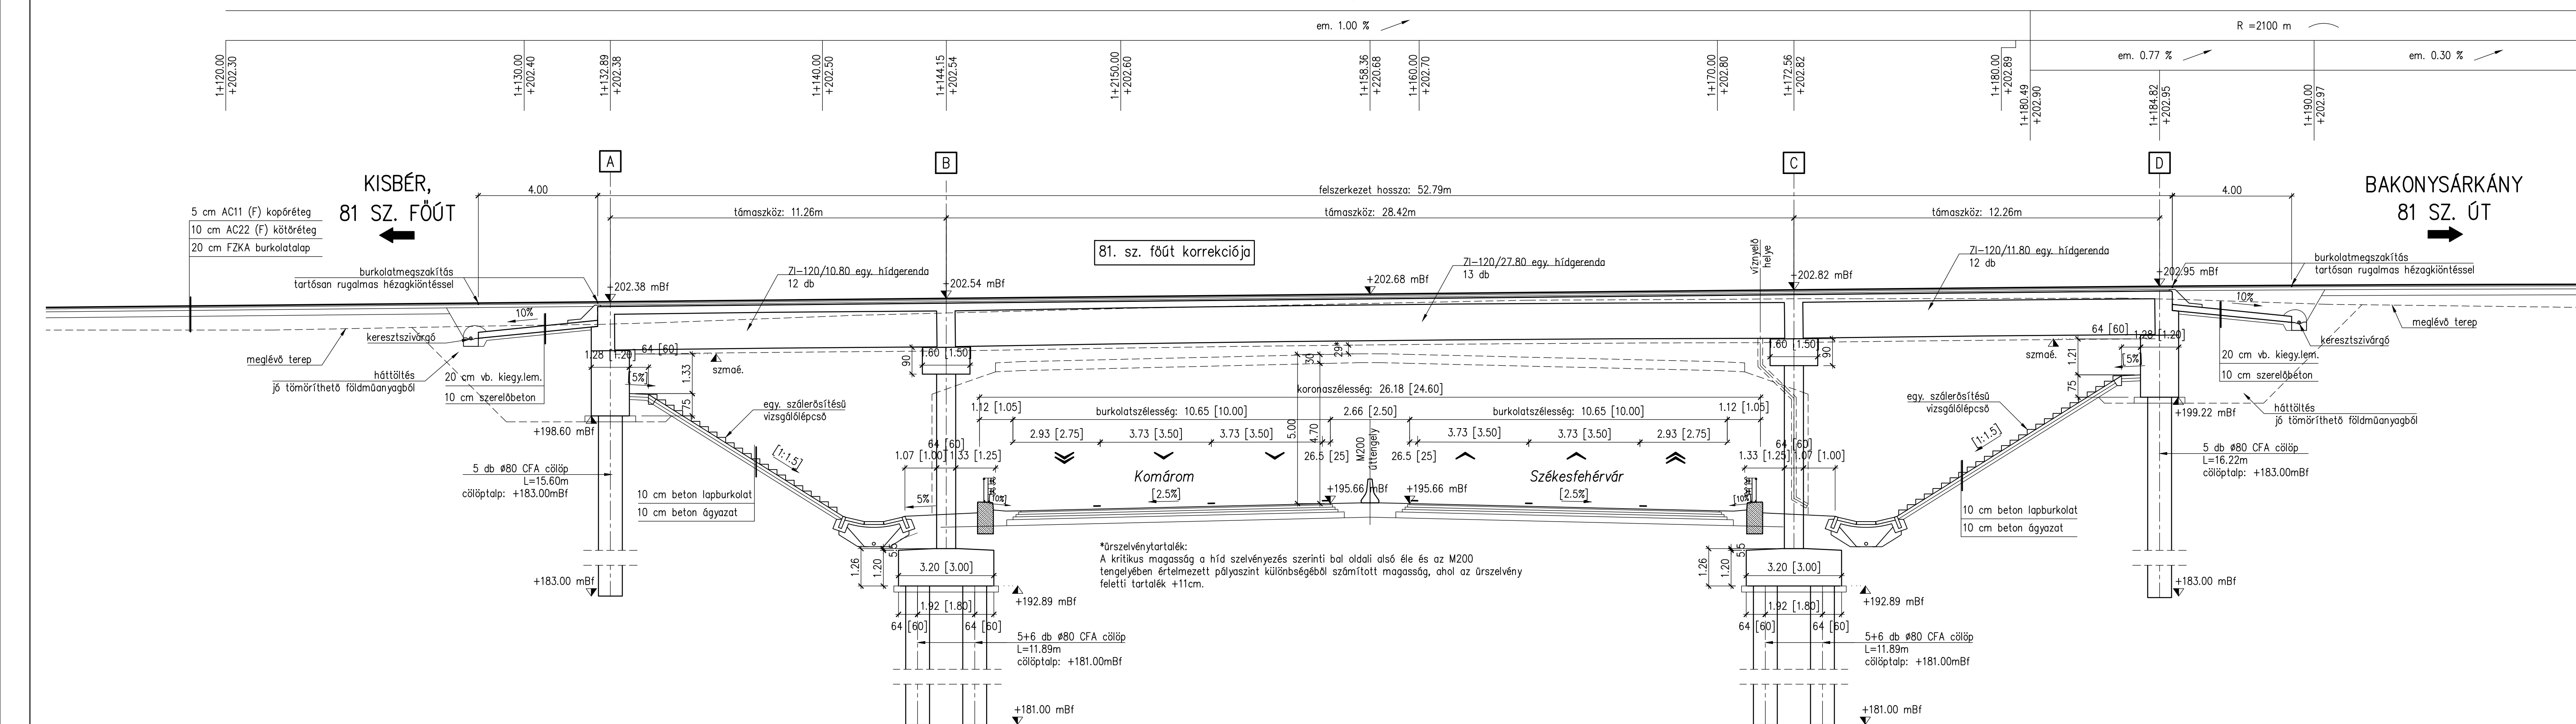


KERESZTMETSZET M 1:50

KÖZBENSŐ NYÍLÁS

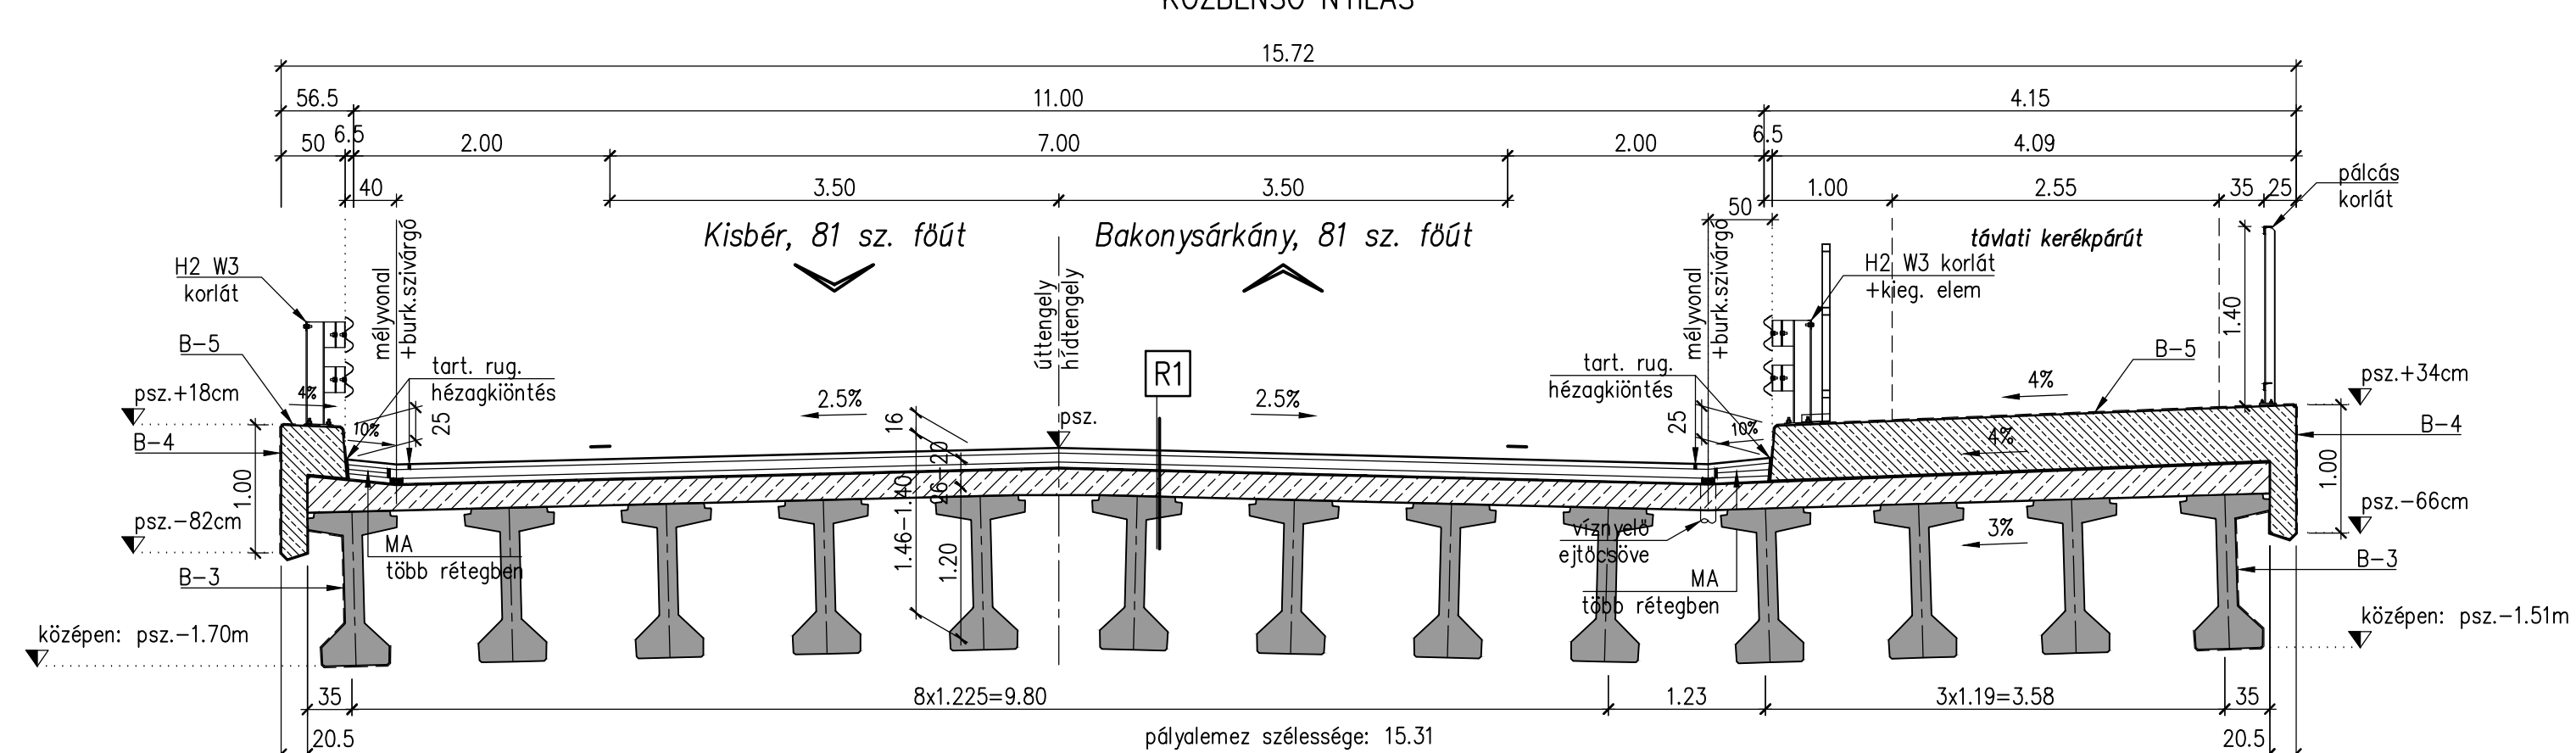

KERESZTMETSZET M 1:50


SZÉLSŐ NYÍLÁS

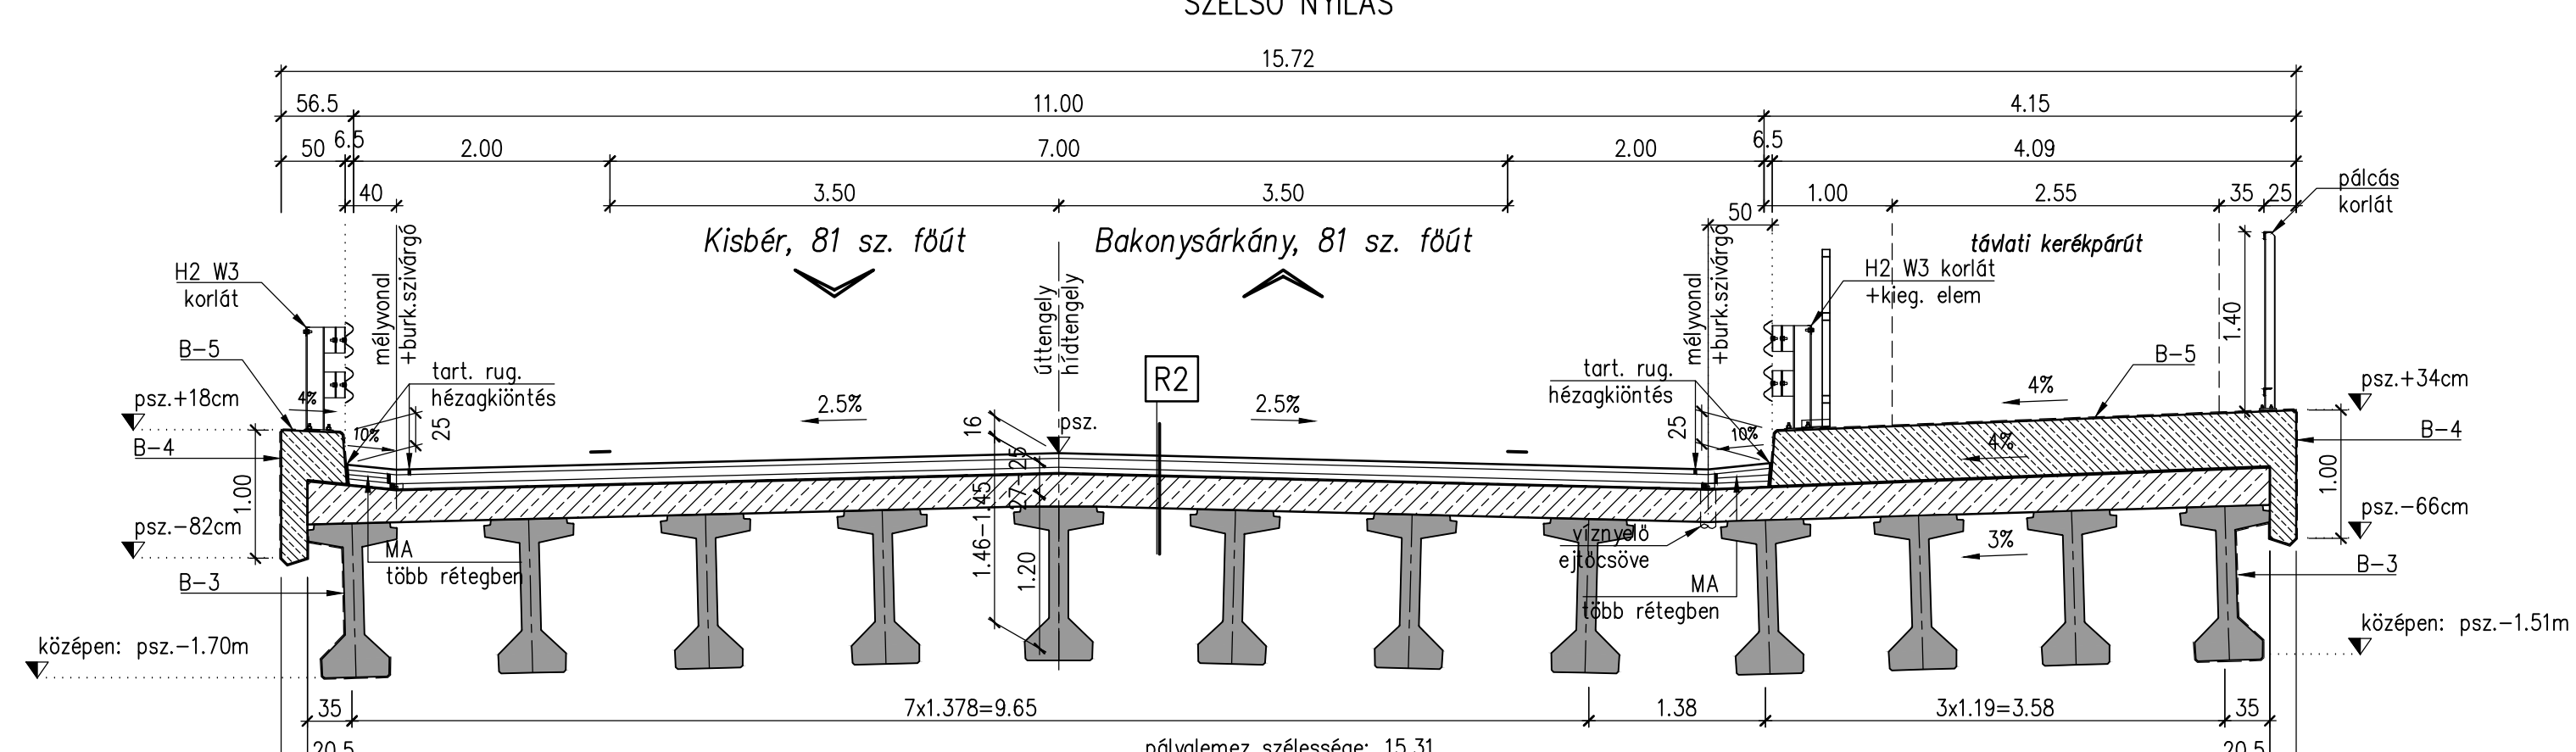

"C" JELŰ PILLER NÉZET M 1:100

[]-es értékek mérőleges hosszak


(α=70°)

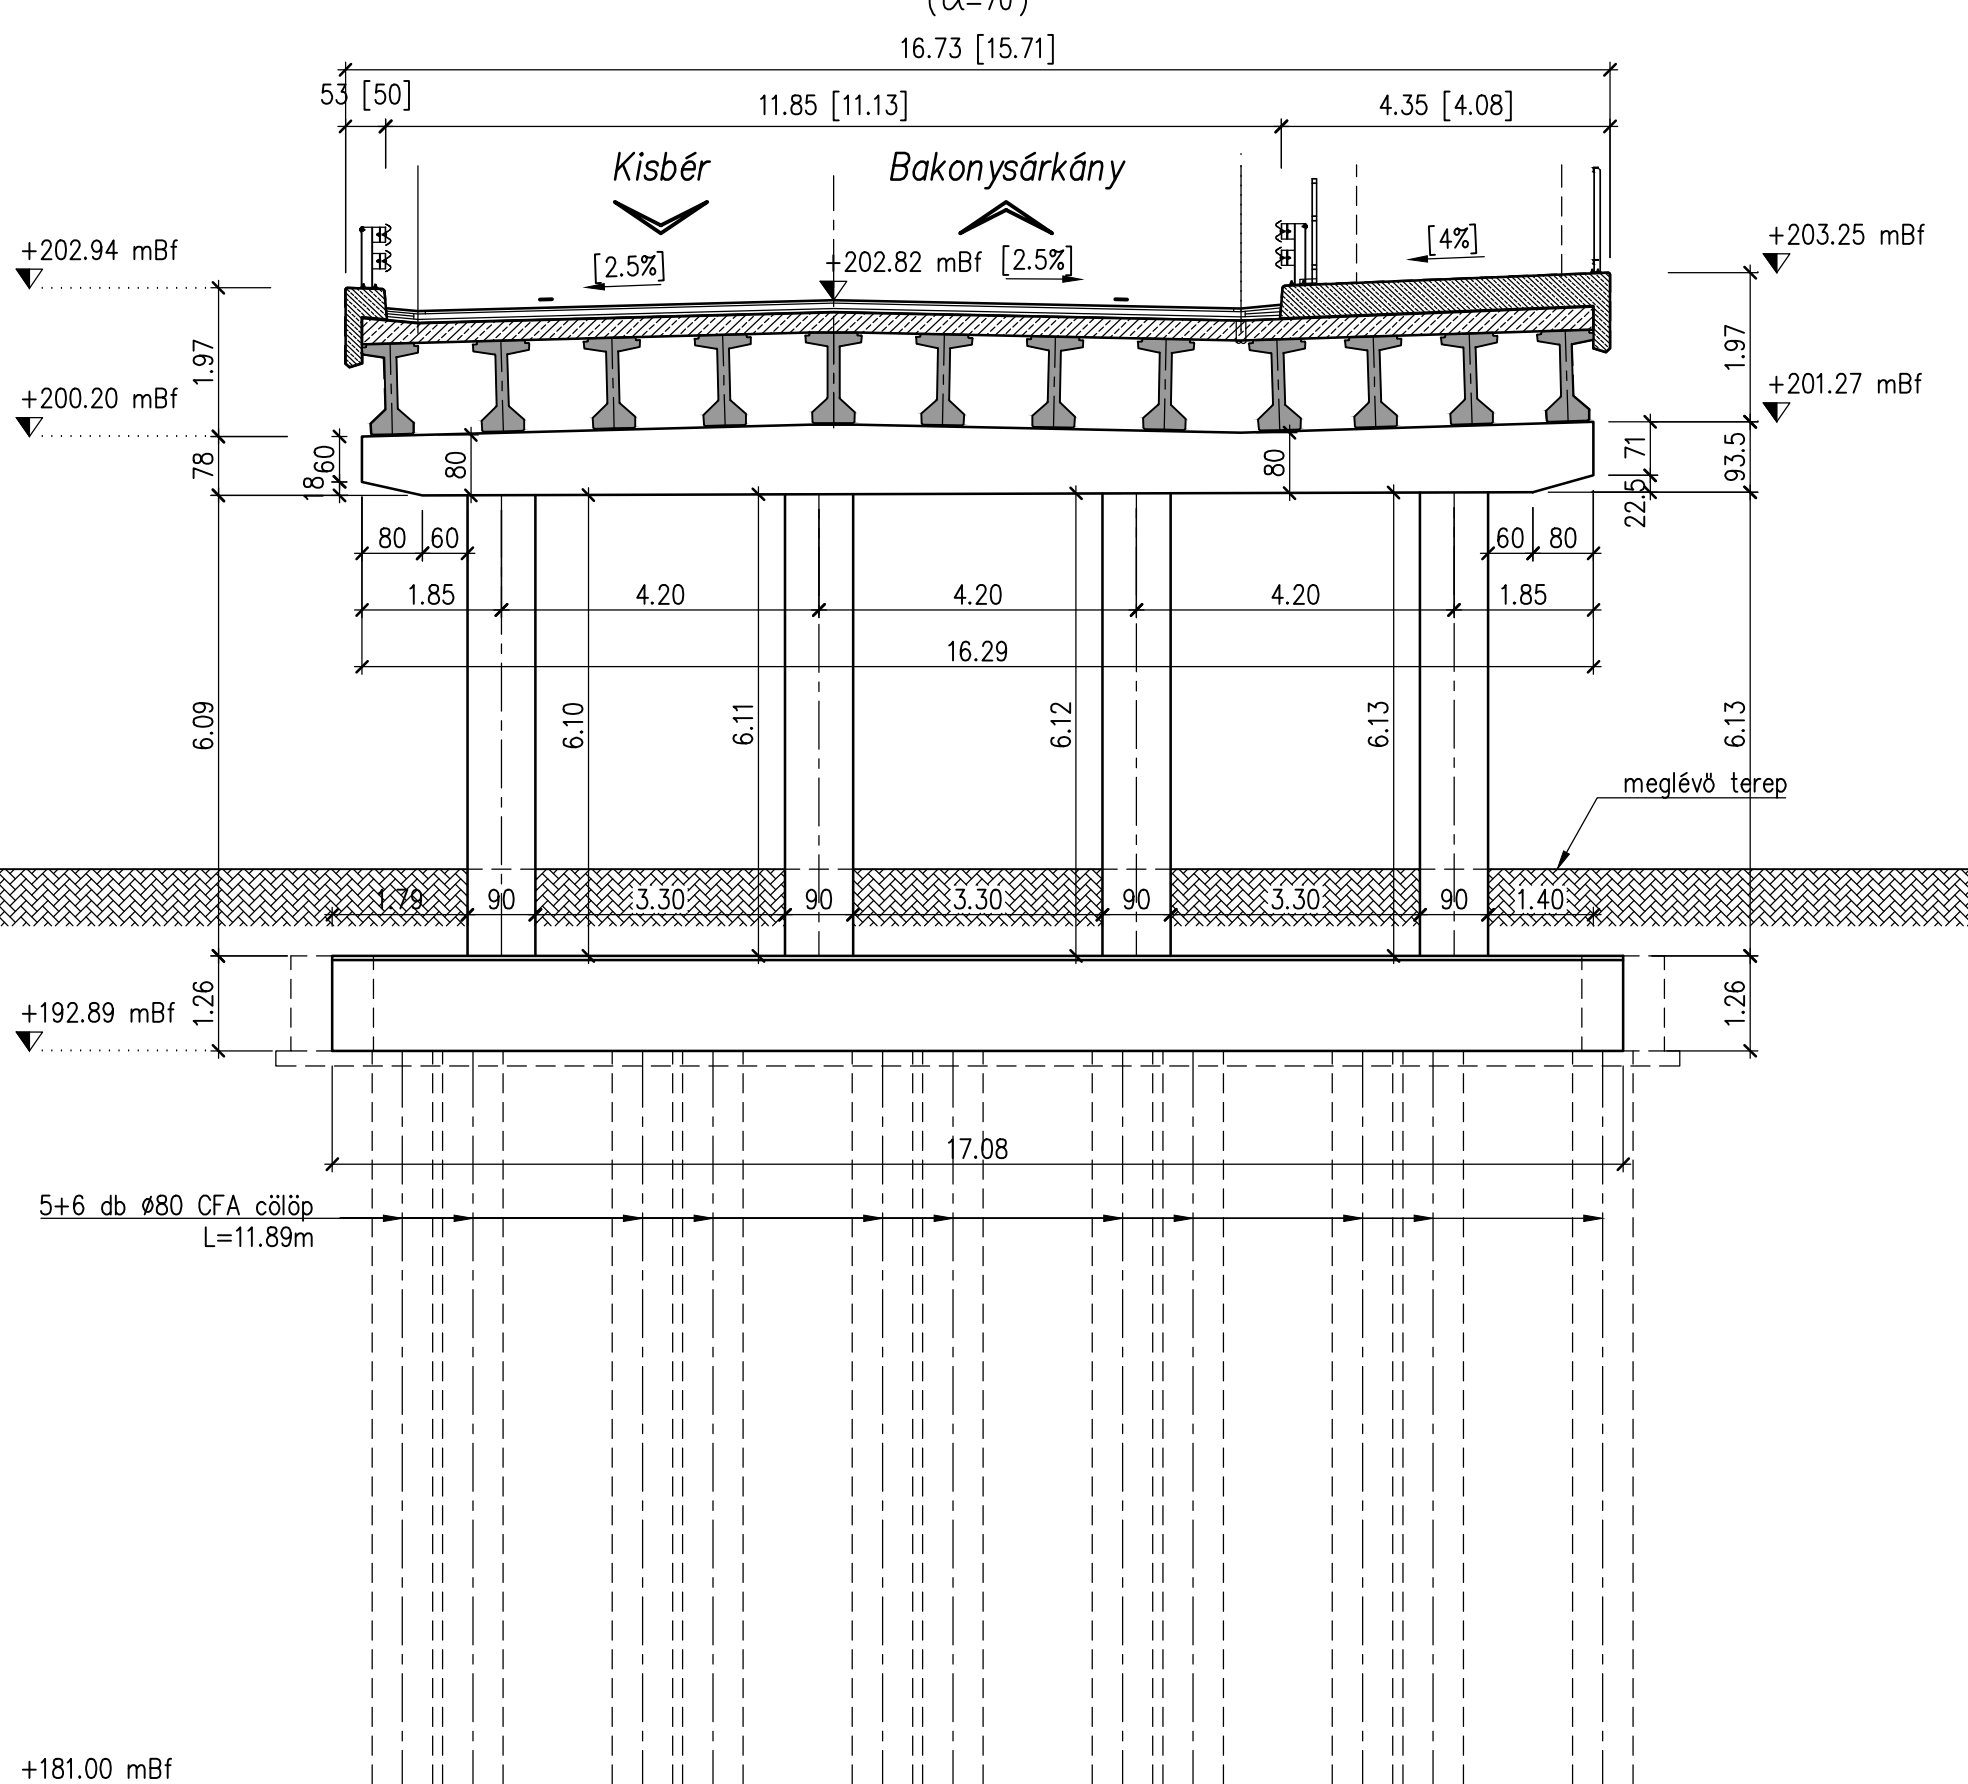

"D" JELŰ HÍDFŐ NÉZET M 1:100

[]-es értékek mérőleges hosszak

(α=70°)

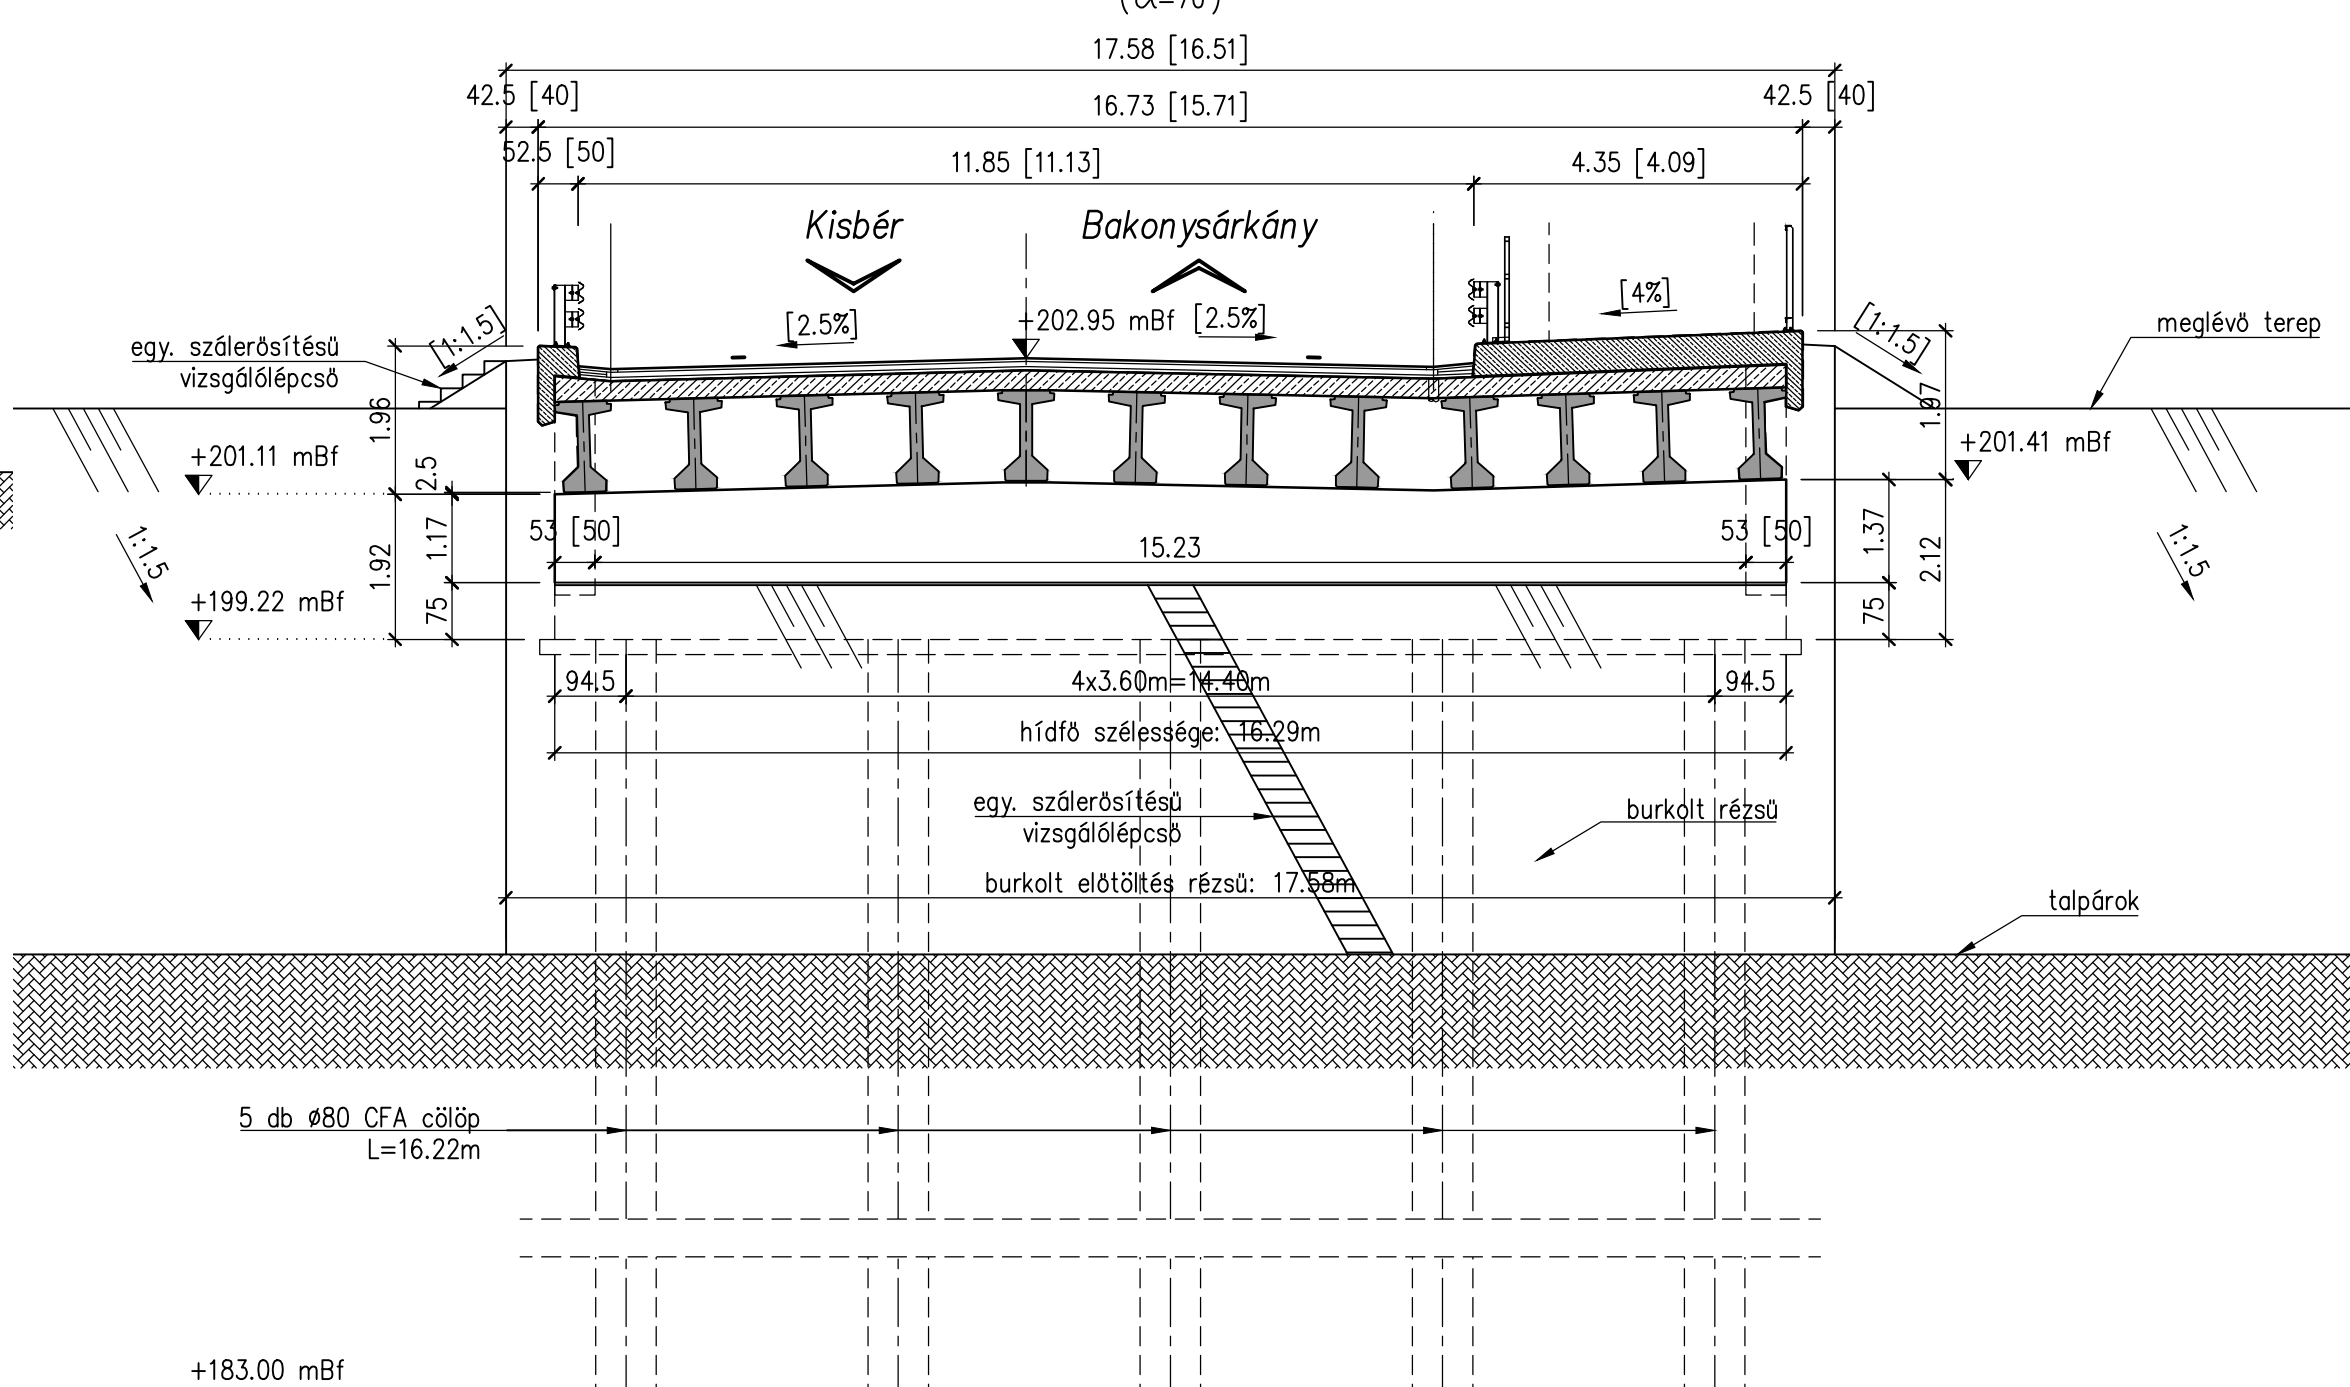

MEGJEGYZÉSEK

- A magasságok EOMA alapokra vonatkoznak.
- A hídvezetékbe bevezető és támaszfőlet magassági méripontot kell bebetonozni az e-ÚT 08.01.25 számú helyen - földre vasozva.
- Magassági méripont jele
- Magassági alapot kell létesíteni minden hid 50 m-es körzetében a híd megépítése után, - a Keresővel egyeztetett helyen - földre vasozva.
- Az avari hidatöréseket tűzvesztéssel kell ellátni. A horganybeton vastagsága min. 85mm.
- A látható vasbeton szerkezeteket el kell látni a tűzvesztéssel kell ellátni (az UME: e-ÚT 07.04.13.2011 alapján):

B-5 beavatattal (korábban az ÚT 2.2.206 szerinti B1) elítélendő felület:

Dokumentum repedéshatárát vagy vándorvonalát, azaz a körvonalát jelölve:

- szegély közepén felül és felül felül a burkolat alsó szélénél mélyre [1-3]
- beton padkák, pótpadkák felül és felül felül a temp alól 30 cm-rel mélyre [1-3]
- pillérválasz szegély felül felül a temp alól 30 cm-rel mélyre [1-3]

B-4 beavatattal (korábban az ÚT 2.2.206 szerinti B3) elítélendő felület:

Körvonalat repedéshatárát vagy vándorvonalát jelölve, azaz a körvonalát jelölve:

- beton padkák, pótpadkák felül felül a temp alól 30 cm-rel mélyre [1-3]
- pillérválasz szegély felül felül a temp alól 30 cm-rel mélyre [1-3]
- közös vasbeton pillér teljes felület a temp alól 30 cm-rel mélyre [1-3]
- hidak és szármak kioldóvezeték közötti lánc felület a temp alól 30 cm-rel mélyre [1-3]
- legfelső vasbeton pillér teljes felület a temp alól 30 cm-rel mélyre [1-3]
- hidak és szármak kioldóvezeték közötti lánc felület a temp alól 30 cm-rel mélyre [1-3]
- A vasút vasútján feletti nyílások a felszerkezt teljes felület, teljes szélességben.
- szármak kioldóvezeték [1-3]
- Körvonalat jelölve, azaz a körvonalát jelölve [1-3]


B-3 beavatattal (korábban az ÚT 2.2.206 szerinti B2) elítélendő felület:

Mérőleges repedéshatárát vagy vándorvonalát jelölve, azaz a körvonalát jelölve:

- előregyártott tartós felszerkezt szélénél, kényszerítő alól 10-15 cm-rel mélyre [1-3]

GEOTECHNIKAI FELTÁRÁSOK

M 1:200

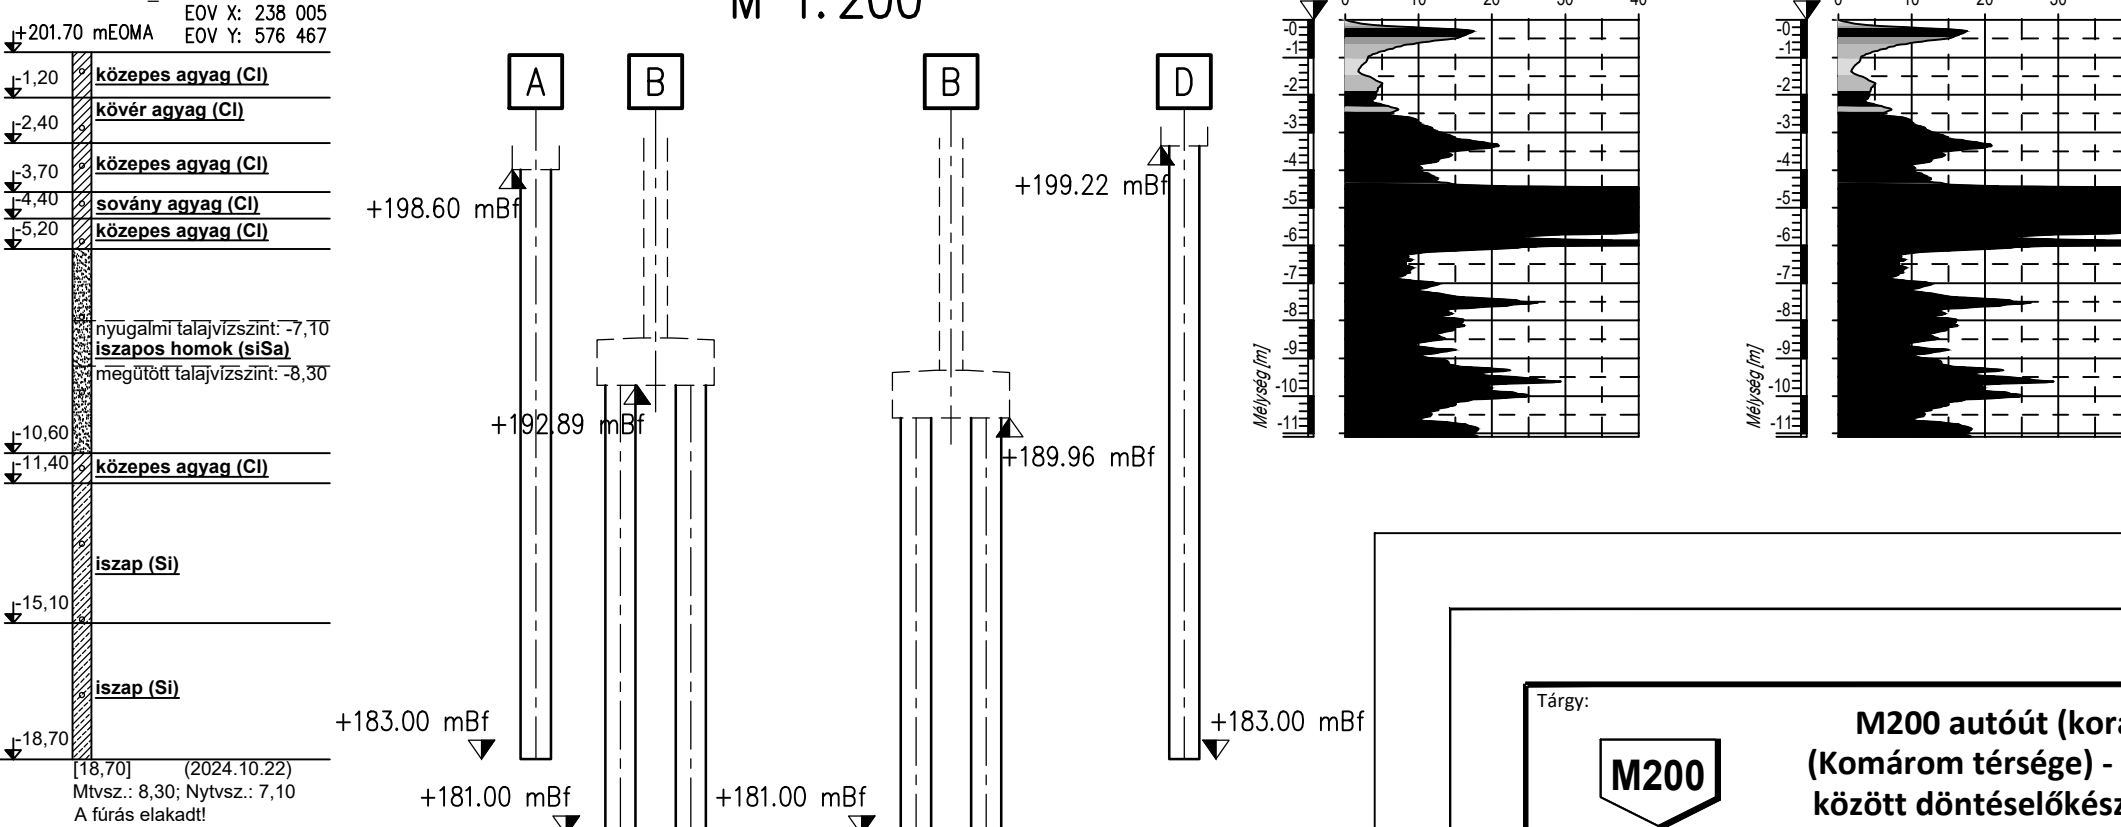

ÁTNÉZÉTI HELYSZÍNRAJZ 1:10000



M200 autót (korábban M81) tervezése az M1 autópálya (Komárom térsége) és M8 gyorsforgalmi út (Sárbogárd térsége) között döntéshozatali tanulmány (DET), KHT és engedélyezési feladata, ajánlat szerinti BIM modell felépítése

Megrendelő: MKIF Magyar Közúti Infrastruktúra Fejlesztő Zrt. Projektkezdési időpont: 2022. 23. 24. Projektidő: 024/2023

Gépjárművezető: KONTÚR Kft. Tervező: 2327

Ügyvezető: Kovács András György Vállalkozás vezető: Mercs György Döntéshozó: Kovács György Projektvezető: 52.700

Szakértő: BMT Mérőközpont Kft. Tervező: BMT-2025-16

Feladat: M200 autót (korábban M81) tervezése az M1 autópálya (Komárom térsége) és M8 gyorsforgalmi út (Sárbogárd térsége) között döntéshozatali tanulmány (DET), KHT és engedélyezési feladata, ajánlat szerinti BIM modell felépítése

Tervező: 2026. május 30. Rajzszám: 02.01

Megjegyzés: M1-200

Általános terv

B225-1. pálya feletti híd az M200 autót 22+555,90 km sz-ban a 81 sz. főút korrekciója átvezetése távlati tervezett kerékpárút átvezetése

Elektronikus azonosító: 22_2017.02.01_E_V05